


SCHEMATIC DRAWING OF SEWAGE TREATMENT PLANT - (MBR TYPE)

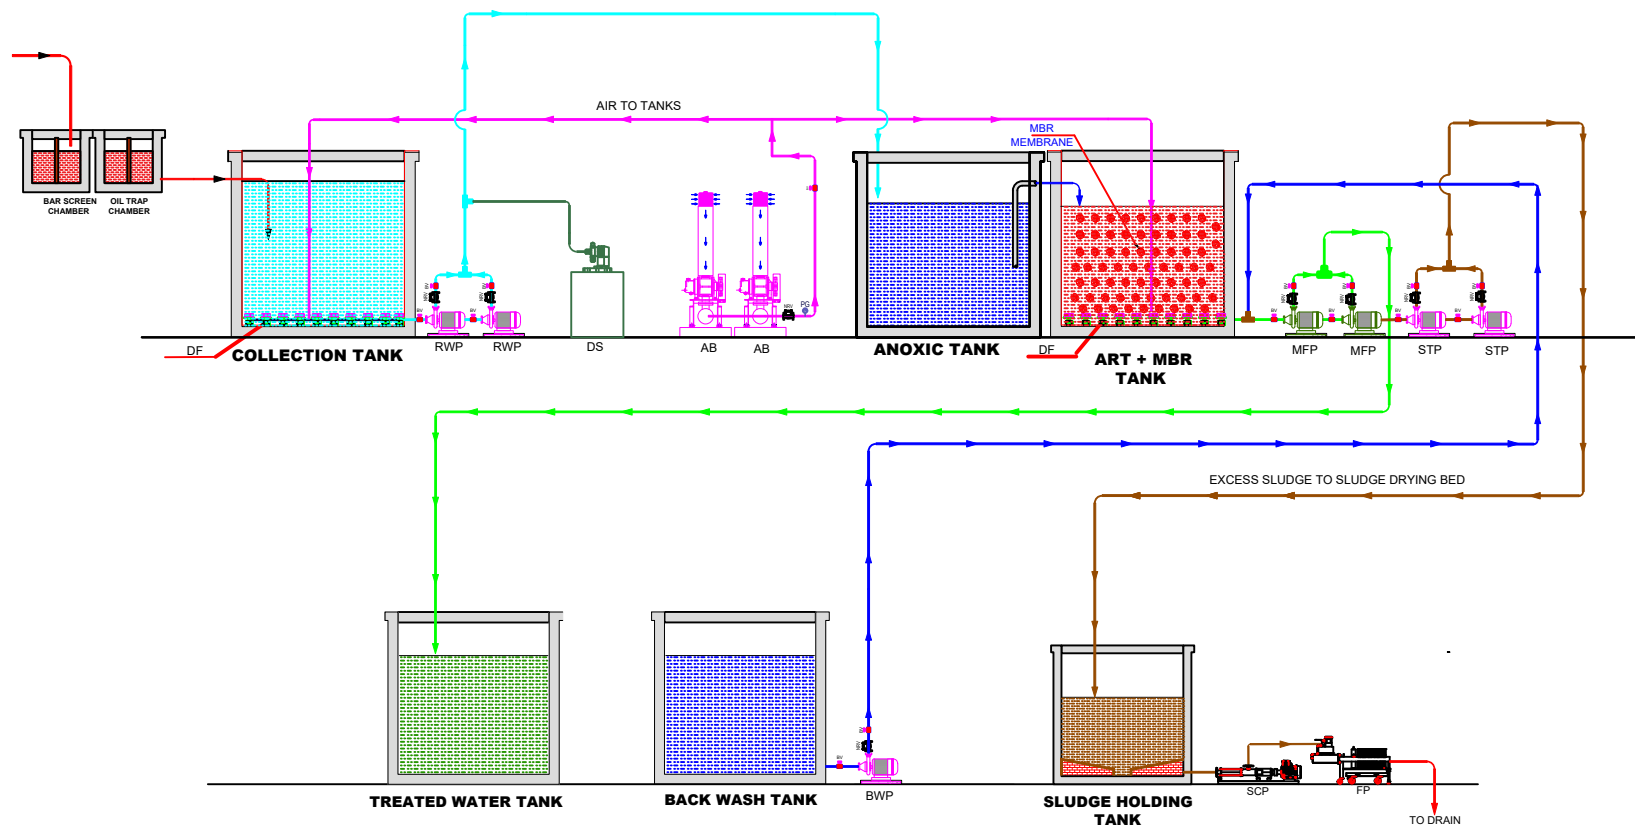

LEGENDS

S.NO	TAG	DESCRIPTION	S.NO	TAG	DESCRIPTION	S.NO	TAG	DESCRIPTION	S.NO	TAG	DESCRIPTION
1.	BSC	BAR SCREEN CHAMBER	7.	BV	BALL VALVE	13.	MFP	MEMBRANE FEED PUMP	19.	BWT	BACK WASH TANK
2.	BC	BAR SCREEN	8.	NRV	NEVER RETURN VALVE	14.	DF	DIFFUSER	20.	SCP	SCREW PUMP
3.	OTC	OIL TRAP CHAMBER	9.	AB	AIR BLOWER	15.	STP	SLUDGE TRANSFER PUMP	21.	FP	FILTER PUMP
4.	CT	COLLECTION TANK	10.	AT	ANOXIC TANK	16.	TWT	TREATED WATER TANK			
5.	RWP	RAW WATER PUMP	11.	MBR	MEMBRANE BIO REACTION TANK	17.	SHT	SLUDGE HOLDING TANK			
6.	DS	DOSING SYSTEM	12.	ART	AERATION TANK	18.	PG	PRESSURE GAUGE			

Design & Manufactured by
Intellect Aqua Private Limited
GROUP OF PRIME AQUA TECH

MailID: design@intellectaqua.com	
DRN	KRISHNARAJA
CHD	BHAVADEEAN
APPD	BOOPATHI
SCALE NTS	
TITLE: SCHEMATIC DRAWING OF STP- MBR	